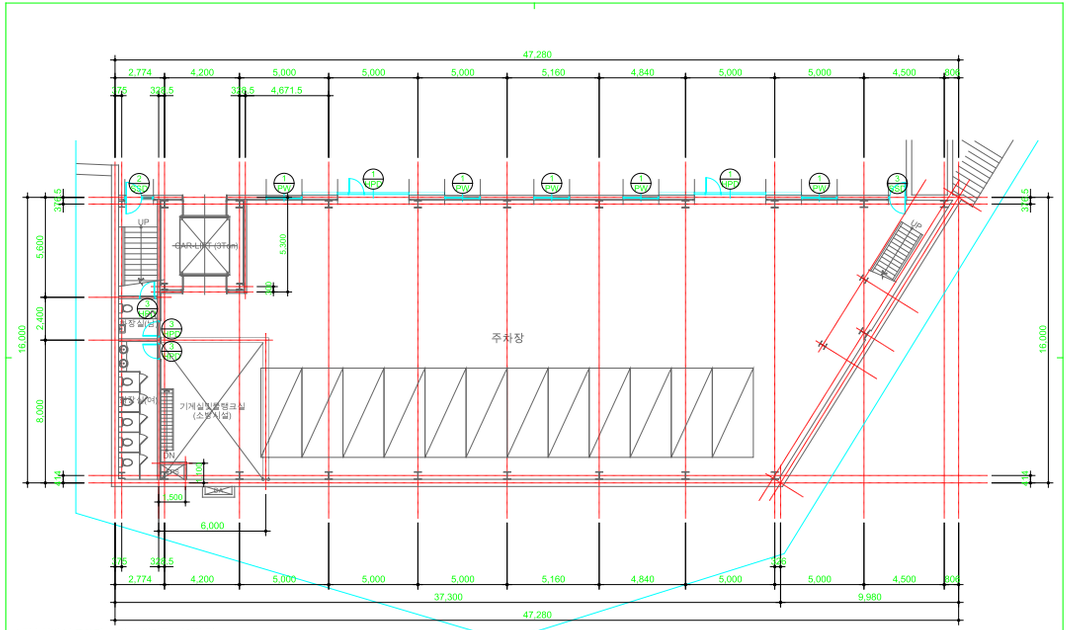

* 절수설비 (수도꼭지, 변기, 샤워기등) 설치할 것
(화장실 등의 바닥은 미끄럼방지 타일을 사용할것)
* 모든창은 열관류률 1.3이하일것, 모든문은 열관류률 1.5이하일것
(사용승인시 창세트 및 문 성적서 제출)
* 건물 외장재료 및 색채 등 시공시 도시디자인팀과 협의할것
(추후 조건 미이행시 사용승인 불가 할수있음)

지하 일층 평 면 도 - 다동

축 척 : 1 / 150

경관, 건축색채 적용
벽 : T-225mm 준불연 판넬 (나등급)
(페인트: 5.8PB 8.0/1.2)
지붕 : T-260mm 준불연 판넬 (나등급)
(페인트: 5.8PB 8.0/1.2)

DS 도시건축사사무소
architectural design
T (051) 943 - 9441 : 정기도 부산시 사하구 다대로 70, 6층 206호 (구랑동)

NO	DATE	REVISION DESCRIPTION	DRWN	CHKJD	APPD

PROJECT TITLE 작품명 | APPROVED BY 승인 | CHKJD BY | SCALE 축척 | DRAWING 도면명 | B.C.C NO | JOB NO | REV NO
DESIGNED BY 작제 | CHKJD BY | DATE 일자 | DRWN BY | DRWG NO 도면번호 | SHEET NO

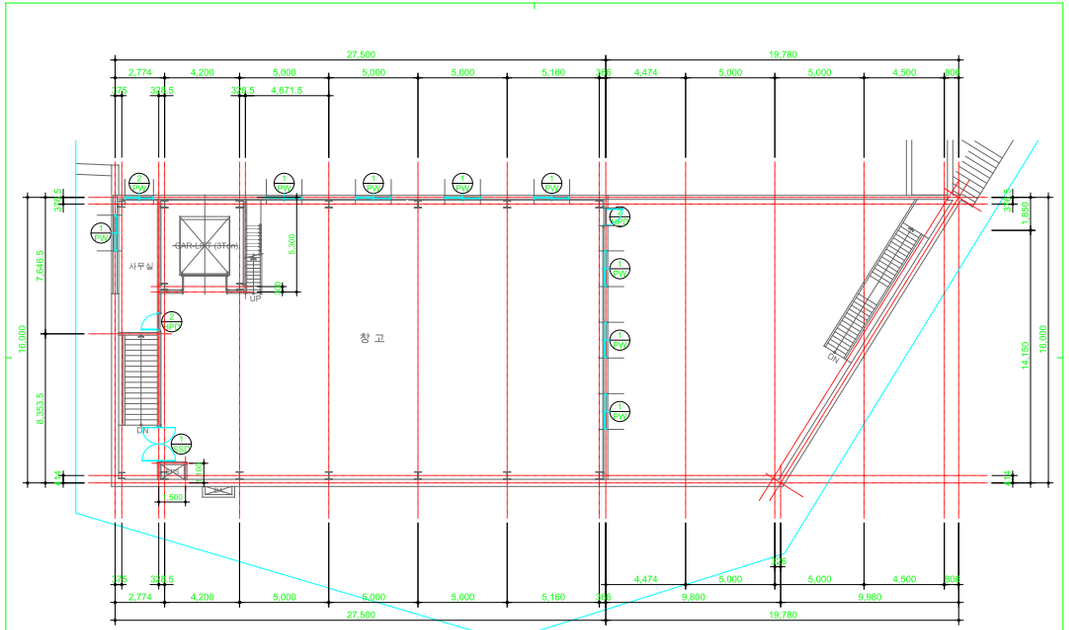

* 절수설비 (수도꼭지, 변기, 샤워기등) 설치할 것
(화장실 등의 바닥은 미끄럼방지 타일을 사용할것)
* 모든창은 열관류률 1.3이하일것, 모든문은 열관류률 1.5이하일것
(사용승인시 창세트 및 문 성적서 제출)
* 건물 외장재료 및 색채 등 시공시 도시디자인팀과 협의할것
(추후 조건 미이행시 사용승인 불가 할수있음)

지상 일층 평 면 도 - 다동

축 척 : 1 / 150

경관, 건축색채 적용
벽 : T-225mm 준불연 판넬 (나등급)
(페인트: 5.8PB 8.0/1.2)
지붕 : T-260mm 준불연 판넬 (나등급)
(페인트: 5.8PB 8.0/1.2)

DS 도시건축사사무소
architectural design
T (051) 943 - 9441 : 정기도 부산시 사하구 다대로 70, 6층 206호 (구랑동)

NO	DATE	REVISION DESCRIPTION	DRWN	CHKJD	APPD

PROJECT TITLE 작품명 | APPROVED BY 승인 | CHKJD BY | SCALE 축척 | DRAWING 도면명 | B.C.C NO | JOB NO | REV NO
DESIGNED BY 작제 | CHKJD BY | DATE 일자 | DRWN BY | DRWG NO 도면번호 | SHEET NO