■ 오수받이 상세도

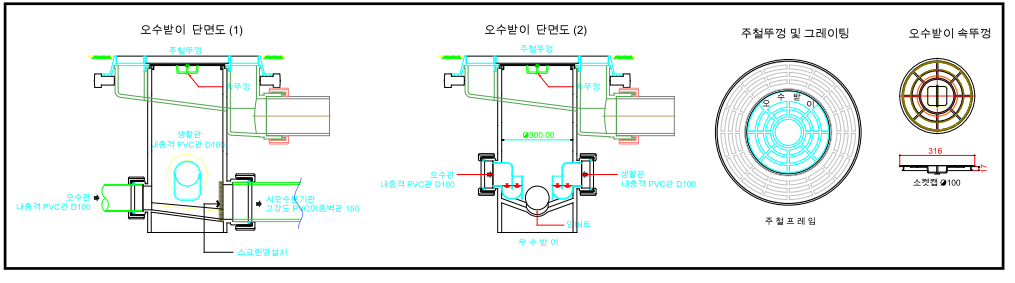

도시 건축사 사무소 Do Si Architecture Engineers 경기도 의정부시 평화로 62, 3층 302호 TEL. (031) 843 - 6661 (새마을 회 맞은편 사거리) FAX. (031) 841 - 7481					PROJECT TITLE. 작품명	APPROVED BY. 승인	CHKLD BY	SCALE. 축척	DRAWING.도면명	B.C.C.NO	JOB NO	REV NO
						DESIGNED BY. 설계	CHKLD BY	DATE. 일자		DRWG NO. 도면번호	SHEET NO.
	NO	DATE	REVISION DESCRIPTION	DRWN	CHKLD	APPD	CHKLD BY	DRWN. BY			