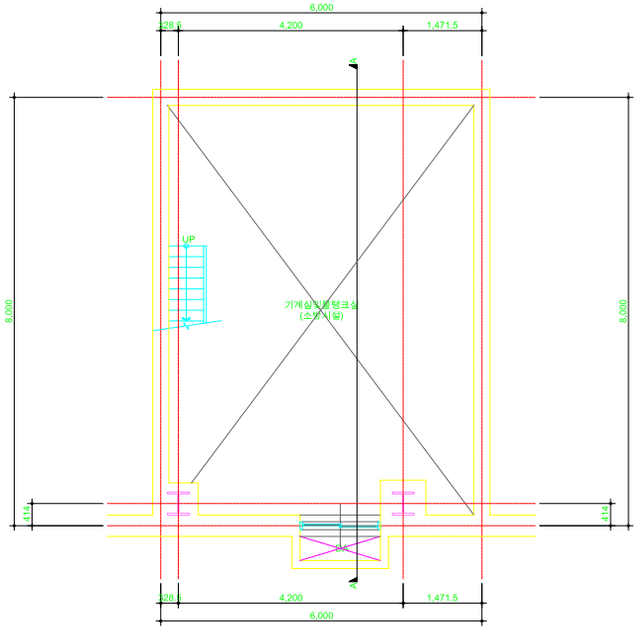

기계실및물탱크실 평면도

축 척 : 1 / 50

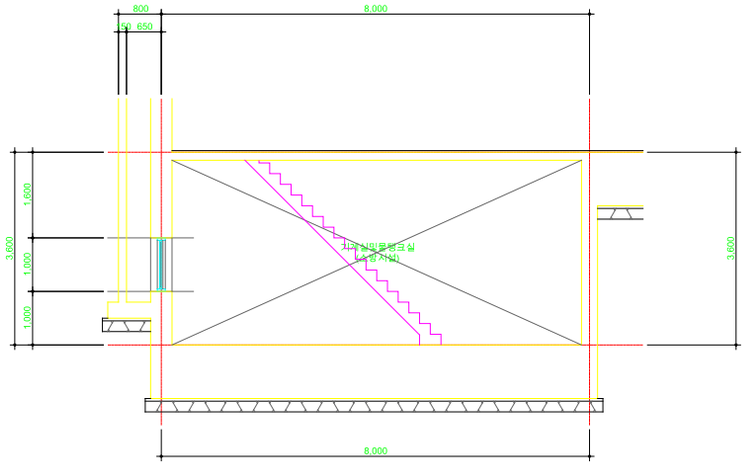

A - A 단 면 도

축 척 : 1 / 50

도시건축사사무소
architectural design
T (031) 943 - 9441 , 031 706 8575 시흥시 시흥로 70, 6층 206호 (은행동)

NO	DATE	REVISION DESCRIPTION	DRWN	CHKD	APPD

PROJECT TITLE 제목명

APPROVED BY 승인 | CHKD BY | SCALE 축척
DESIGNED BY 작제 | CHKD BY | DATE 일자
CHKD BY | DRWN BY

DRAWING 도면명

B.E.C.NO | JOB NO | REV NO
DRWG NO.도면번호 | SHEET NO